


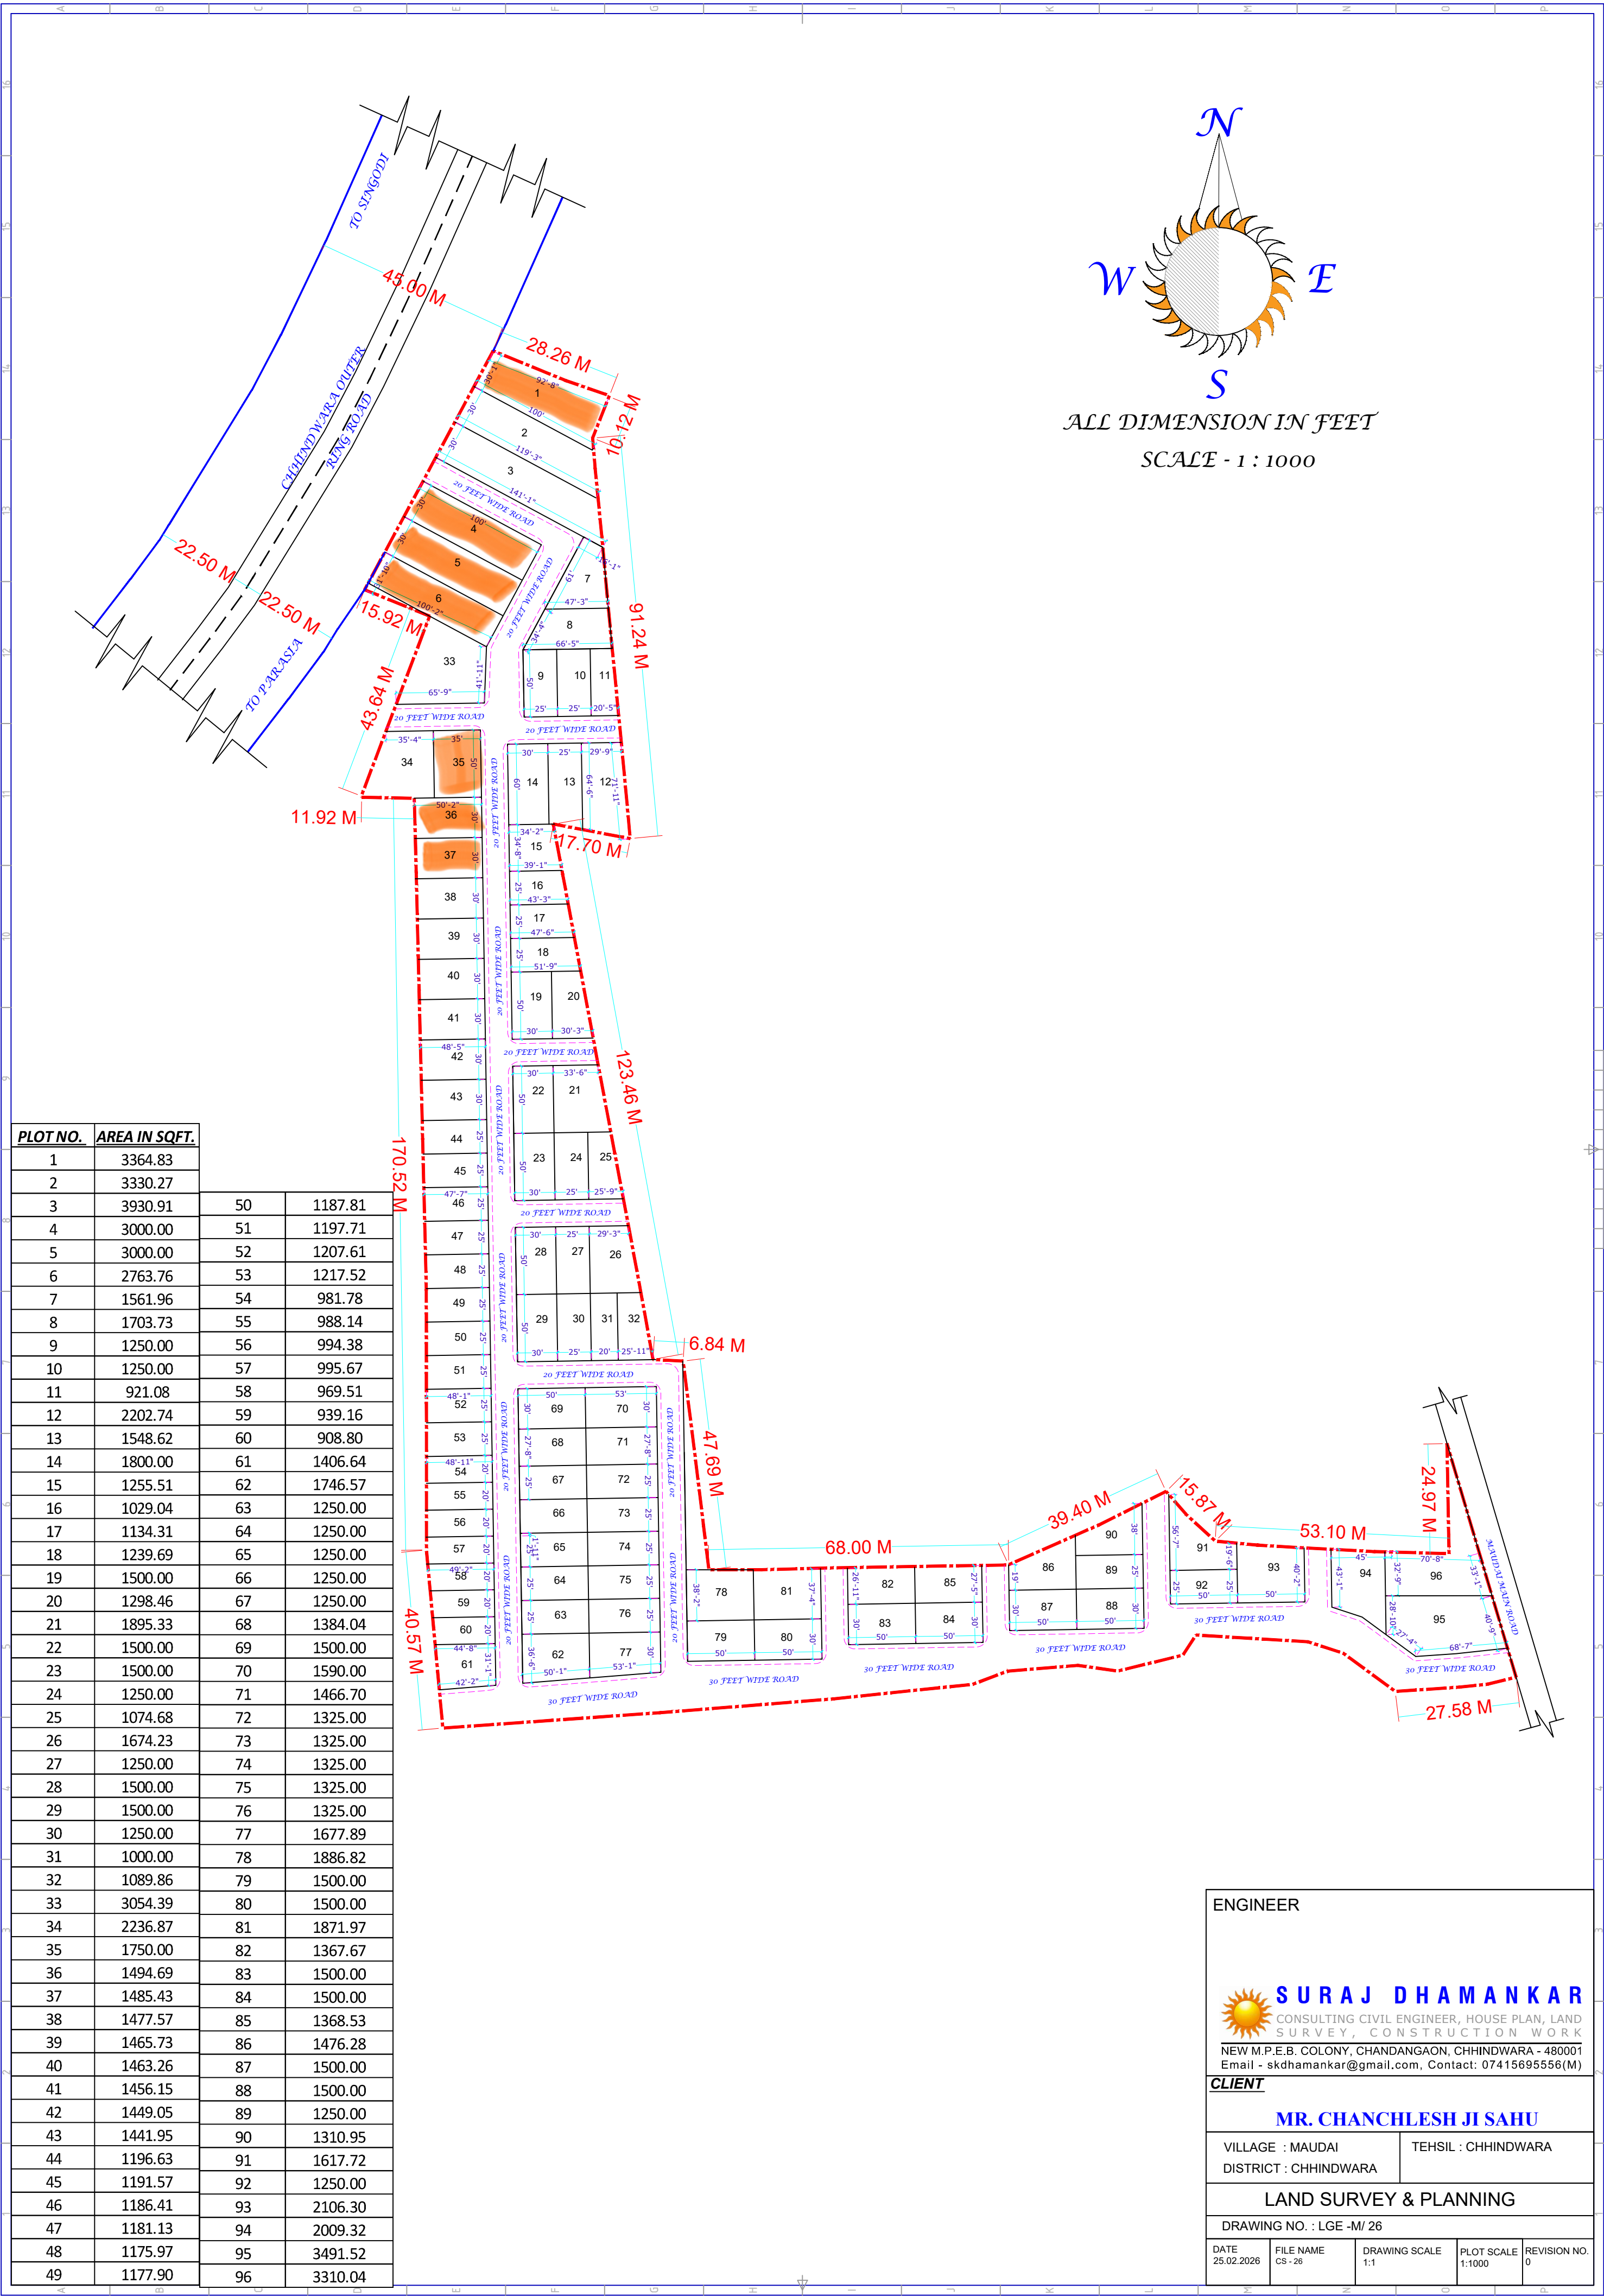

PLOT NO.	AREA IN SQFT.		
1	3364.83		
2	3330.27		
3	3930.91	50	1187.81
4	3000.00	51	1197.71
5	3000.00	52	1207.61
6	2763.76	53	1217.52
7	1561.96	54	981.78
8	1703.73	55	988.14
9	1250.00	56	994.38
10	1250.00	57	995.67
11	921.08	58	969.51
12	2202.74	59	939.16
13	1548.62	60	908.80
14	1800.00	61	1406.64
15	1255.51	62	1746.57
16	1029.04	63	1250.00
17	1134.31	64	1250.00
18	1239.69	65	1250.00
19	1500.00	66	1250.00
20	1298.46	67	1250.00
21	1895.33	68	1384.04
22	1500.00	69	1500.00
23	1500.00	70	1590.00
24	1250.00	71	1466.70
25	1074.68	72	1325.00
26	1674.23	73	1325.00
27	1250.00	74	1325.00
28	1500.00	75	1325.00
29	1500.00	76	1325.00
30	1250.00	77	1677.89
31	1000.00	78	1886.82
32	1089.86	79	1500.00
33	3054.39	80	1500.00
34	2236.87	81	1871.97
35	1750.00	82	1367.67
36	1494.69	83	1500.00
37	1485.43	84	1500.00
38	1477.57	85	1368.53
39	1465.73	86	1476.28
40	1463.26	87	1500.00
41	1456.15	88	1500.00
42	1449.05	89	1250.00
43	1441.95	90	1310.95
44	1196.63	91	1617.72
45	1191.57	92	1250.00
46	1186.41	93	2106.30
47	1181.13	94	2009.32
48	1175.97	95	3491.52
49	1177.90	96	3310.04

ENGINEER

**SURAJ DHAMANKAR**
CONSULTING CIVIL ENGINEER, HOUSE PLAN, LAND SURVEY, CONSTRUCTION WORK
NEW M.P.E.B. COLONY, CHANDANGAON, CHHINDWARA - 480001
Email - skdhamankar@gmail.com, Contact: 07415695556(M)

CLIENT

MR. CHANCHLESH JI SAHU

VILLAGE : MAUDAI TEHSIL : CHHINDWARA
DISTRICT : CHHINDWARA

LAND SURVEY & PLANNING

DRAWING NO. : LGE -M/ 26

DATE 25.02.2026	FILE NAME CS - 26	DRAWING SCALE 1:1	PLOT SCALE 1:1000	REVISION NO. 0
--------------------	----------------------	----------------------	----------------------	-------------------